


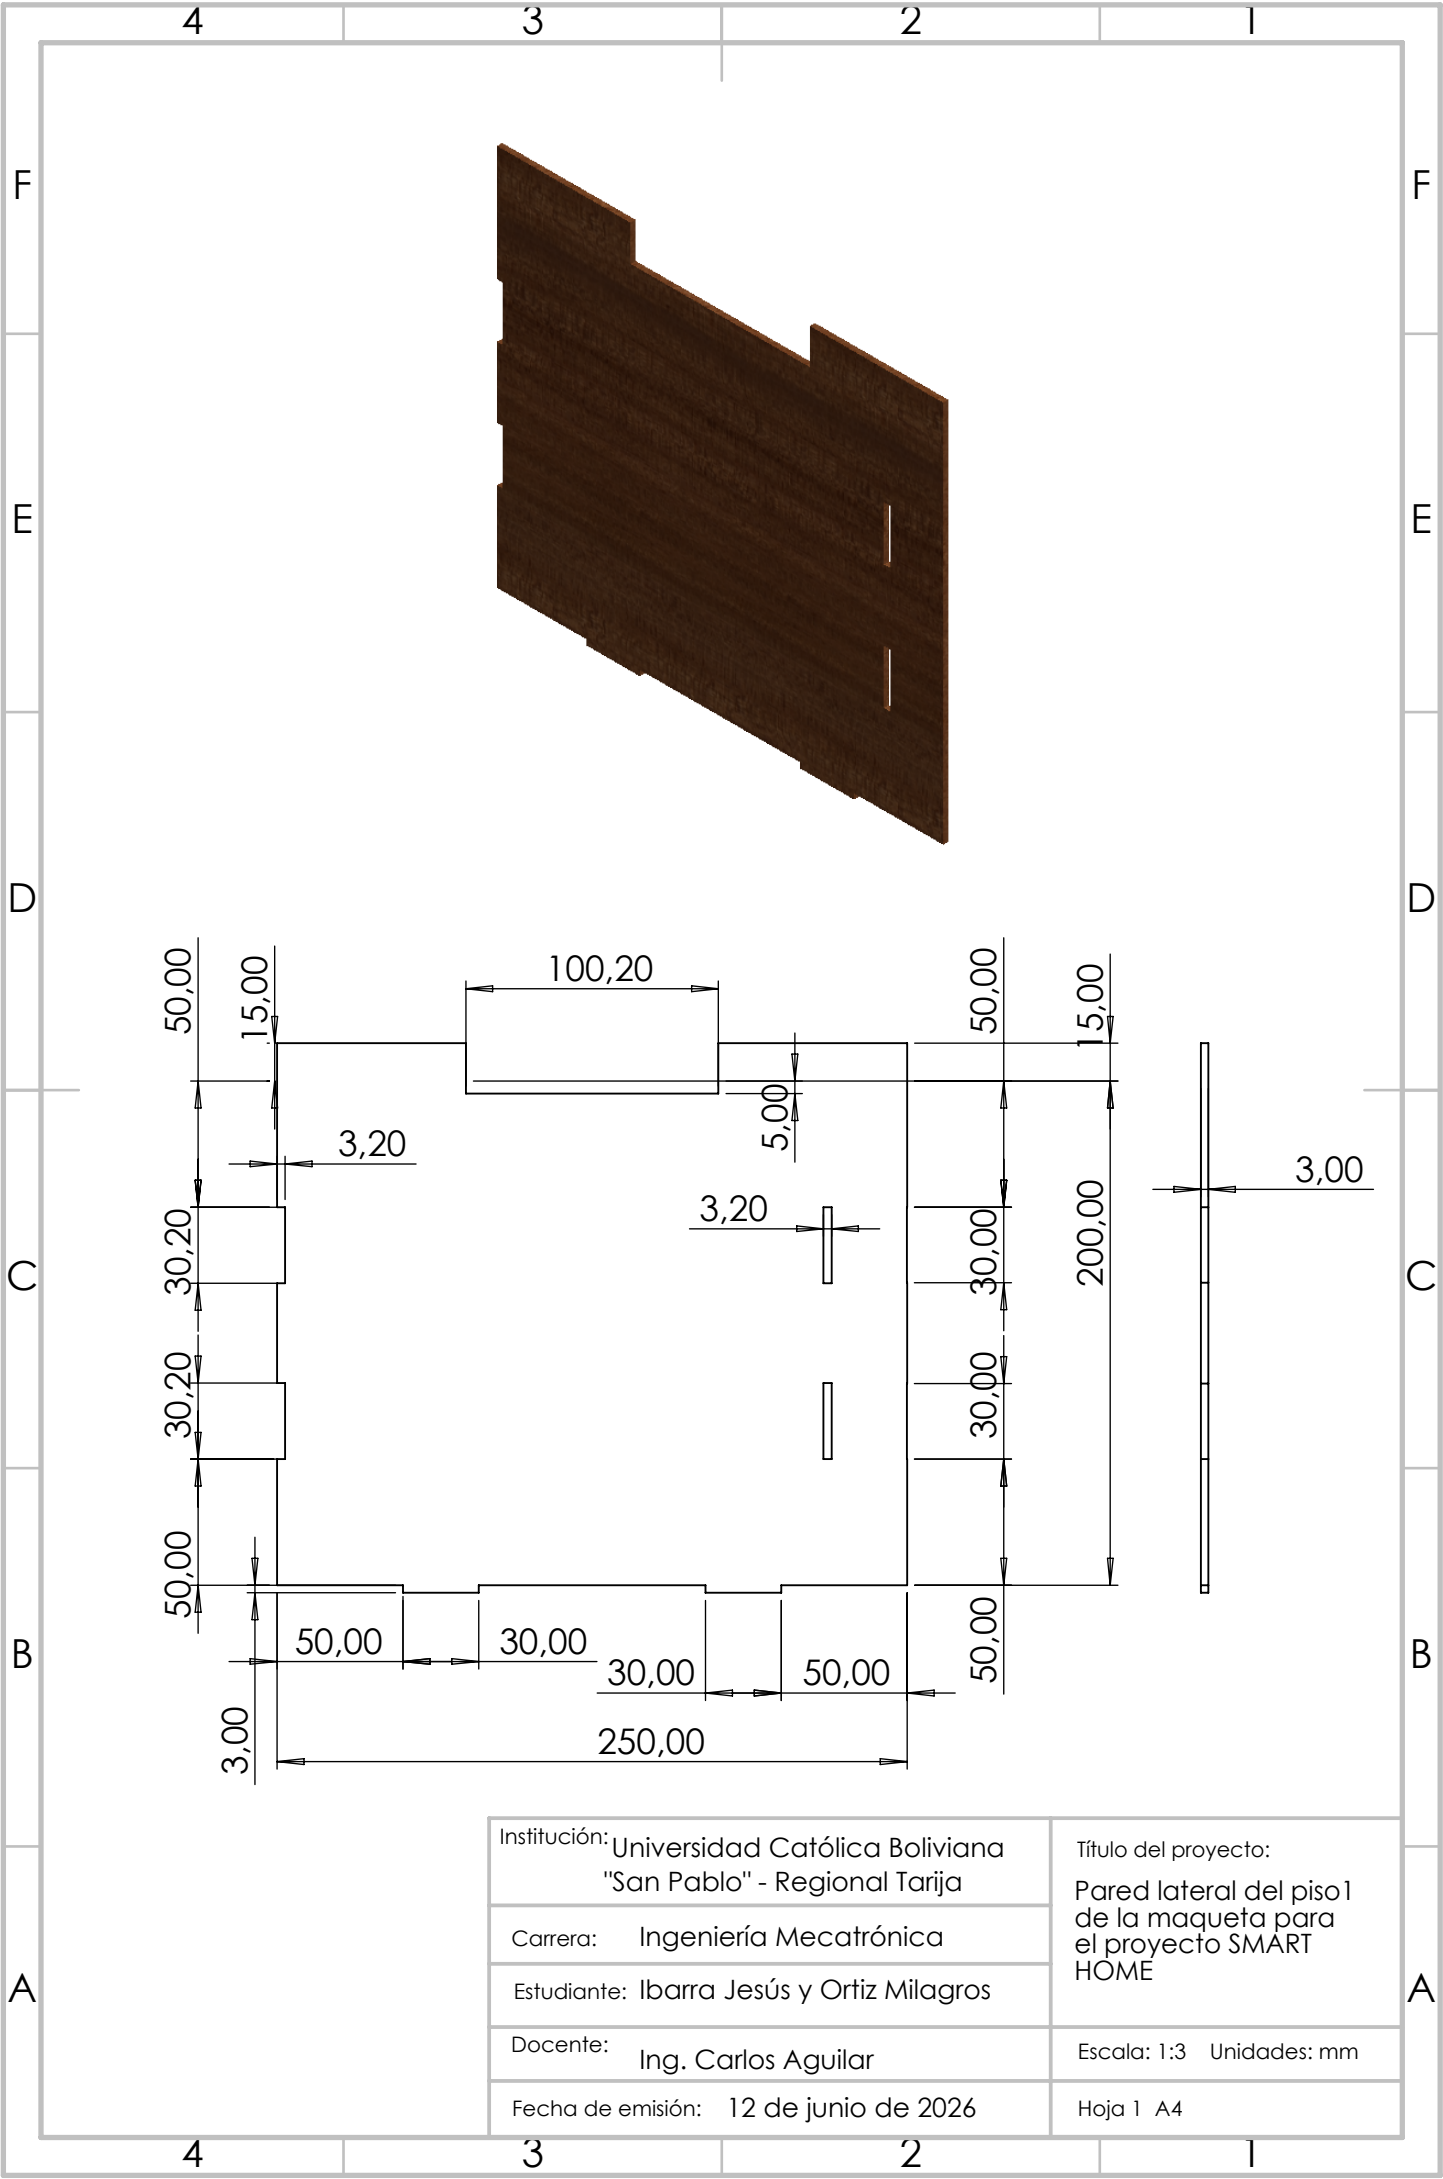

Institución: Universidad Católica Boliviana "San Pablo" - Regional Tarija	Título del proyecto: Pared lateral del piso 1 de la maqueta para el proyecto SMART HOME
Carrera: Ingeniería Mecatrónica	
Estudiante: Ibarra Jesús y Ortiz Milagros	
Docente: Ing. Carlos Aguilar	Escala: 1:3 Unidades: mm
Fecha de emisión: 12 de junio de 2026	Hoja 1 A4