


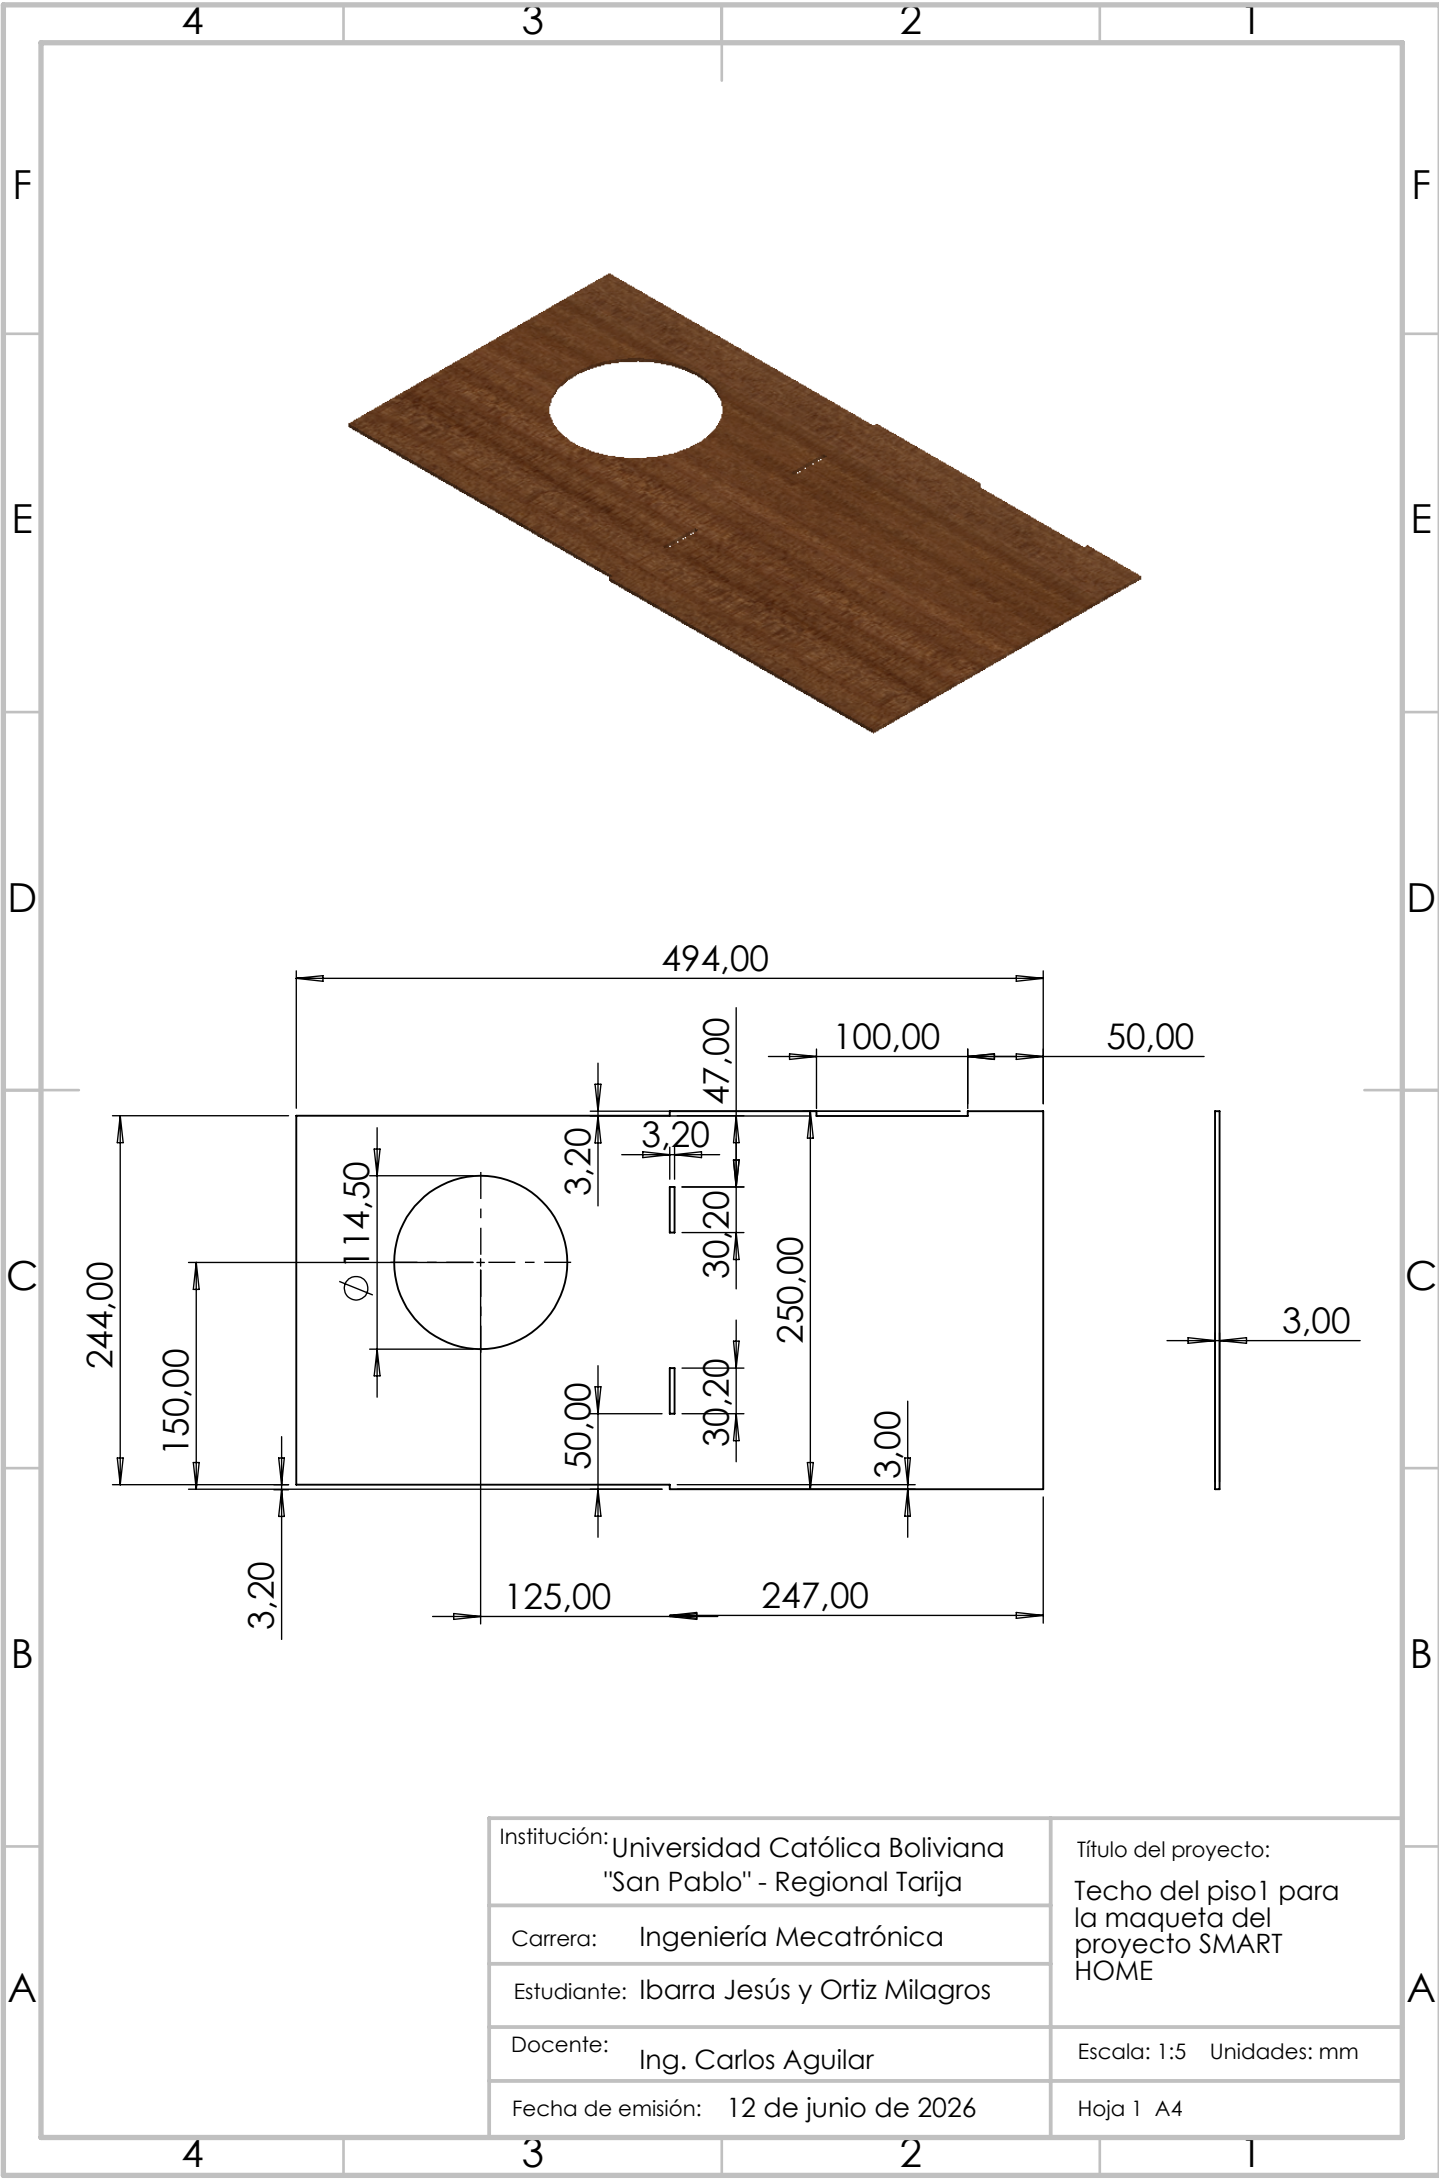

Institución: Universidad Católica Boliviana "San Pablo" - Regional Tarija		Título del proyecto: Techo del piso1 para la maqueta del proyecto SMART HOME
Carrera: Ingeniería Mecatrónica		
Estudiante: Ibarra Jesús y Ortiz Milagros		
Docente: Ing. Carlos Aguilar		Escala: 1:5 Unidades: mm
Fecha de emisión: 12 de junio de 2026		Hoja 1 A4